
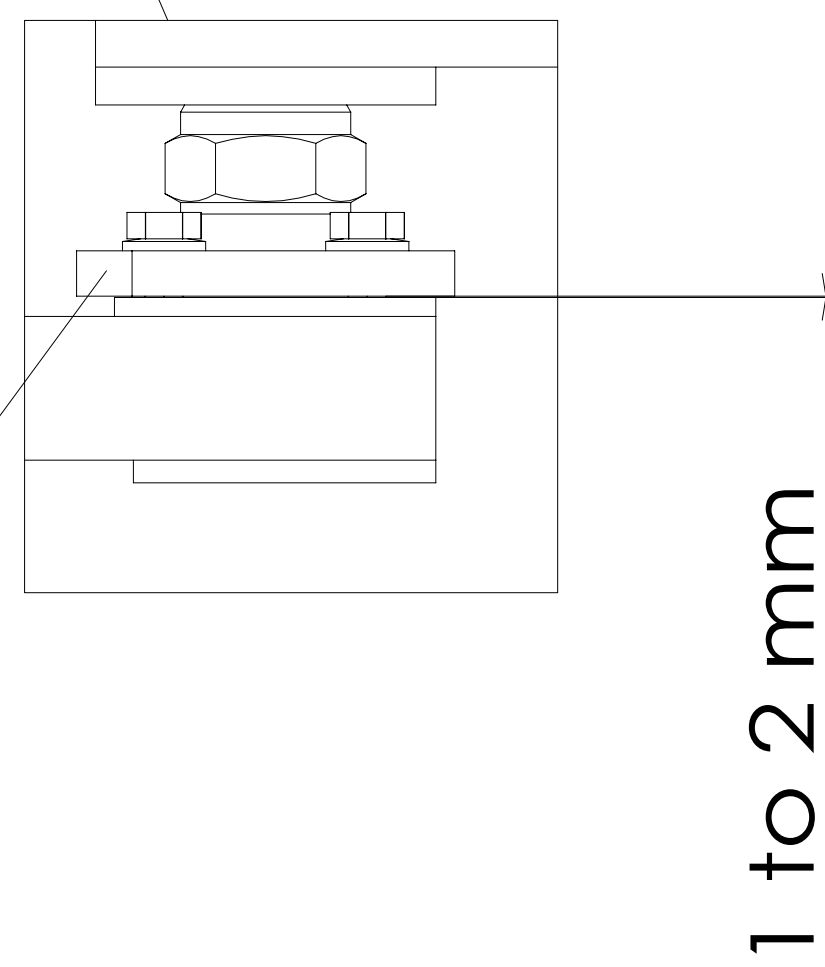
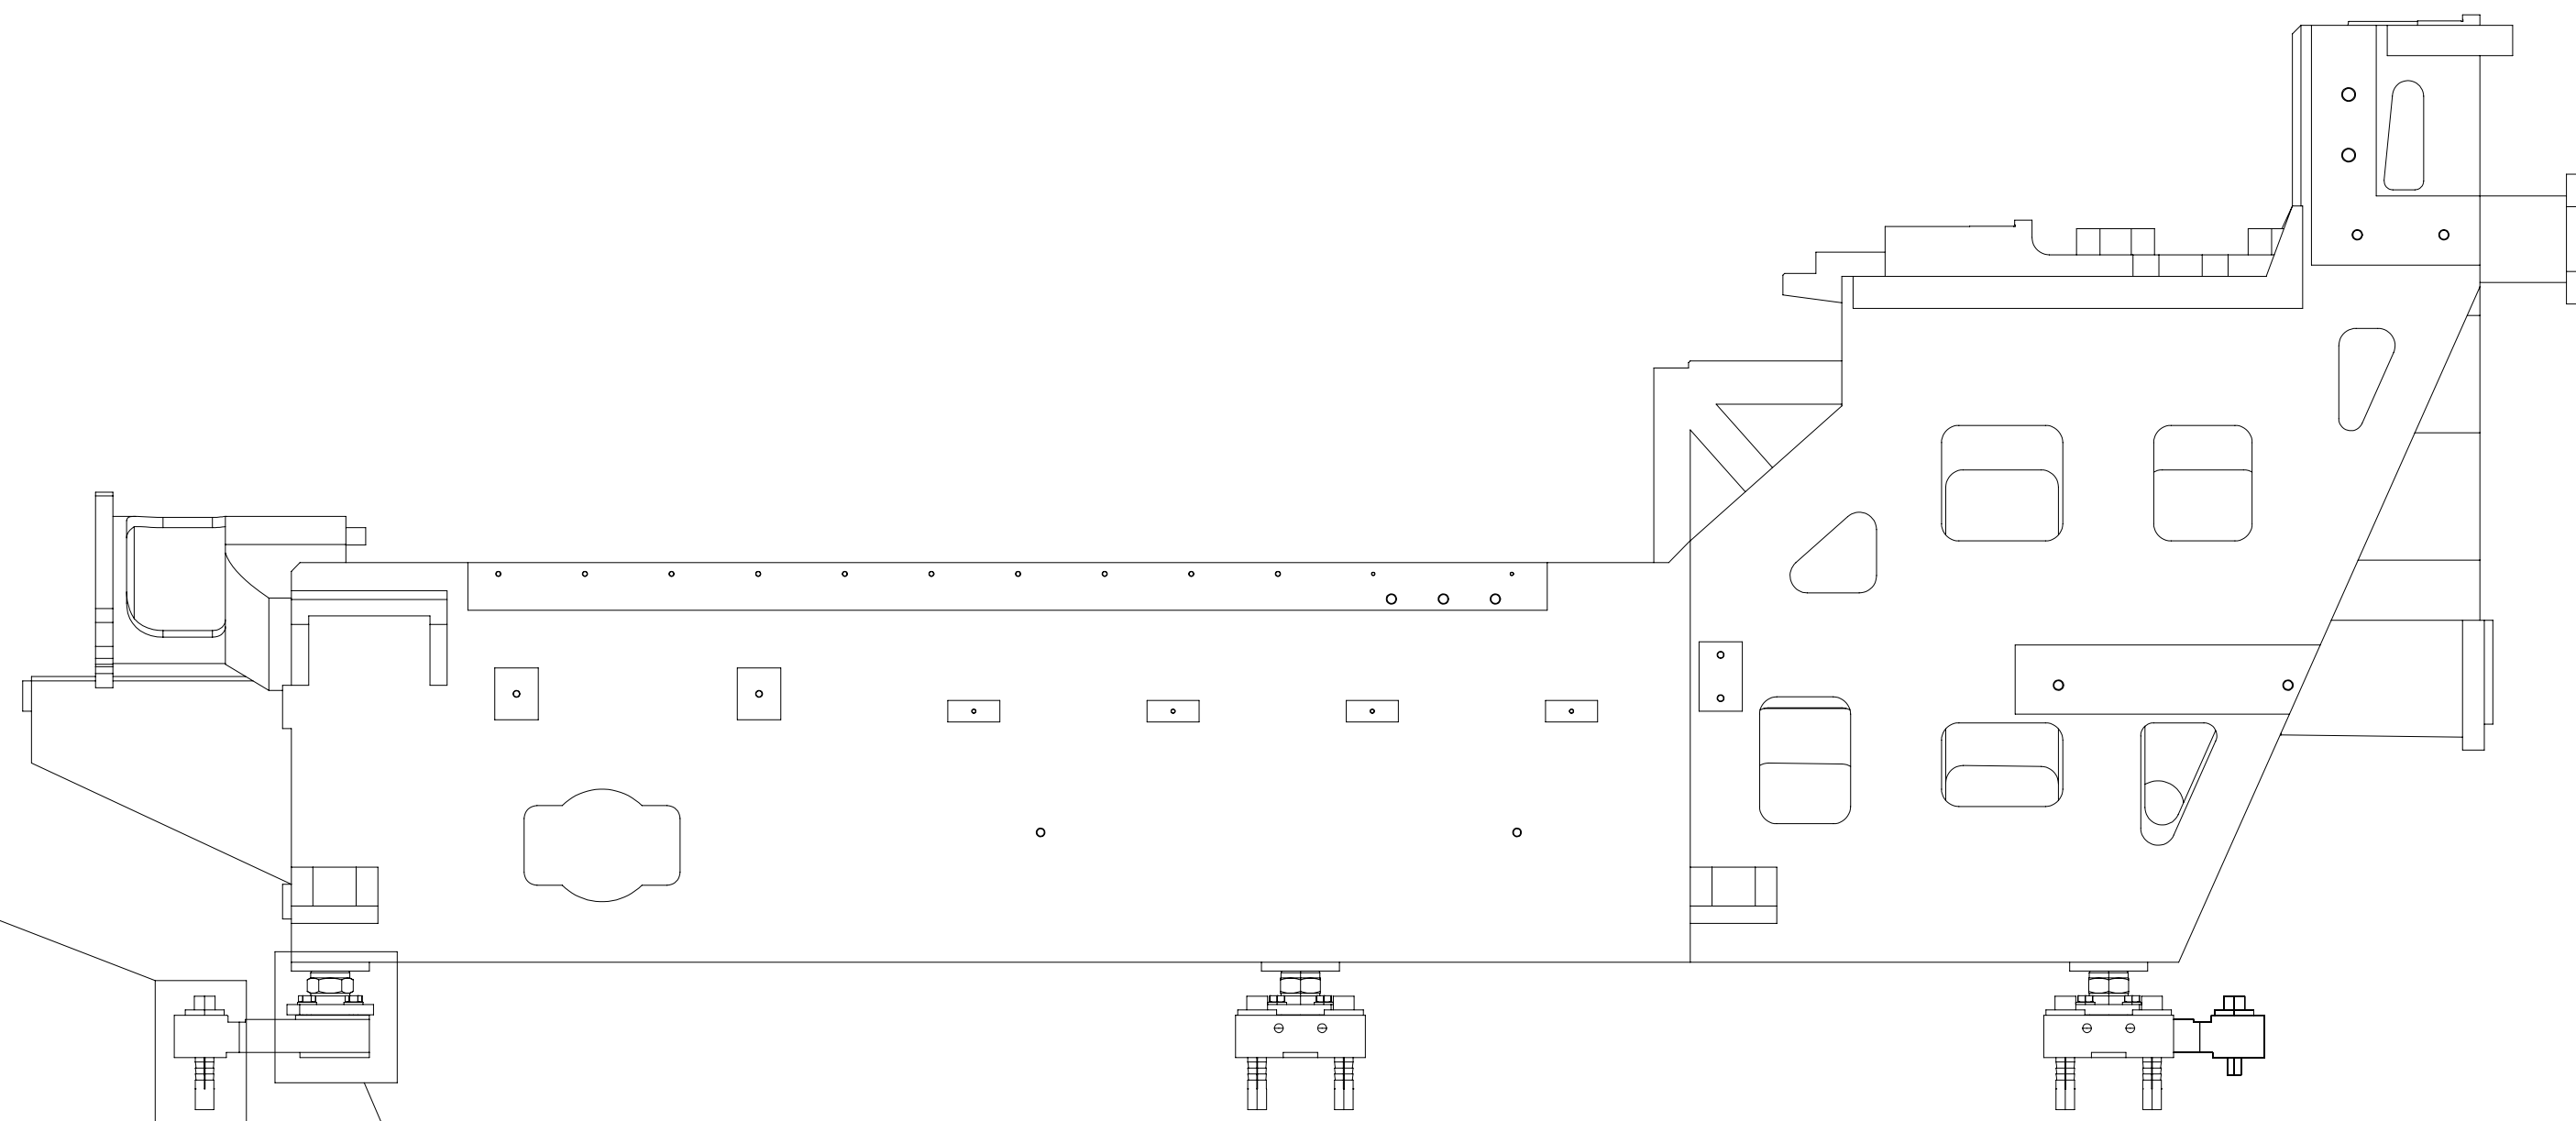
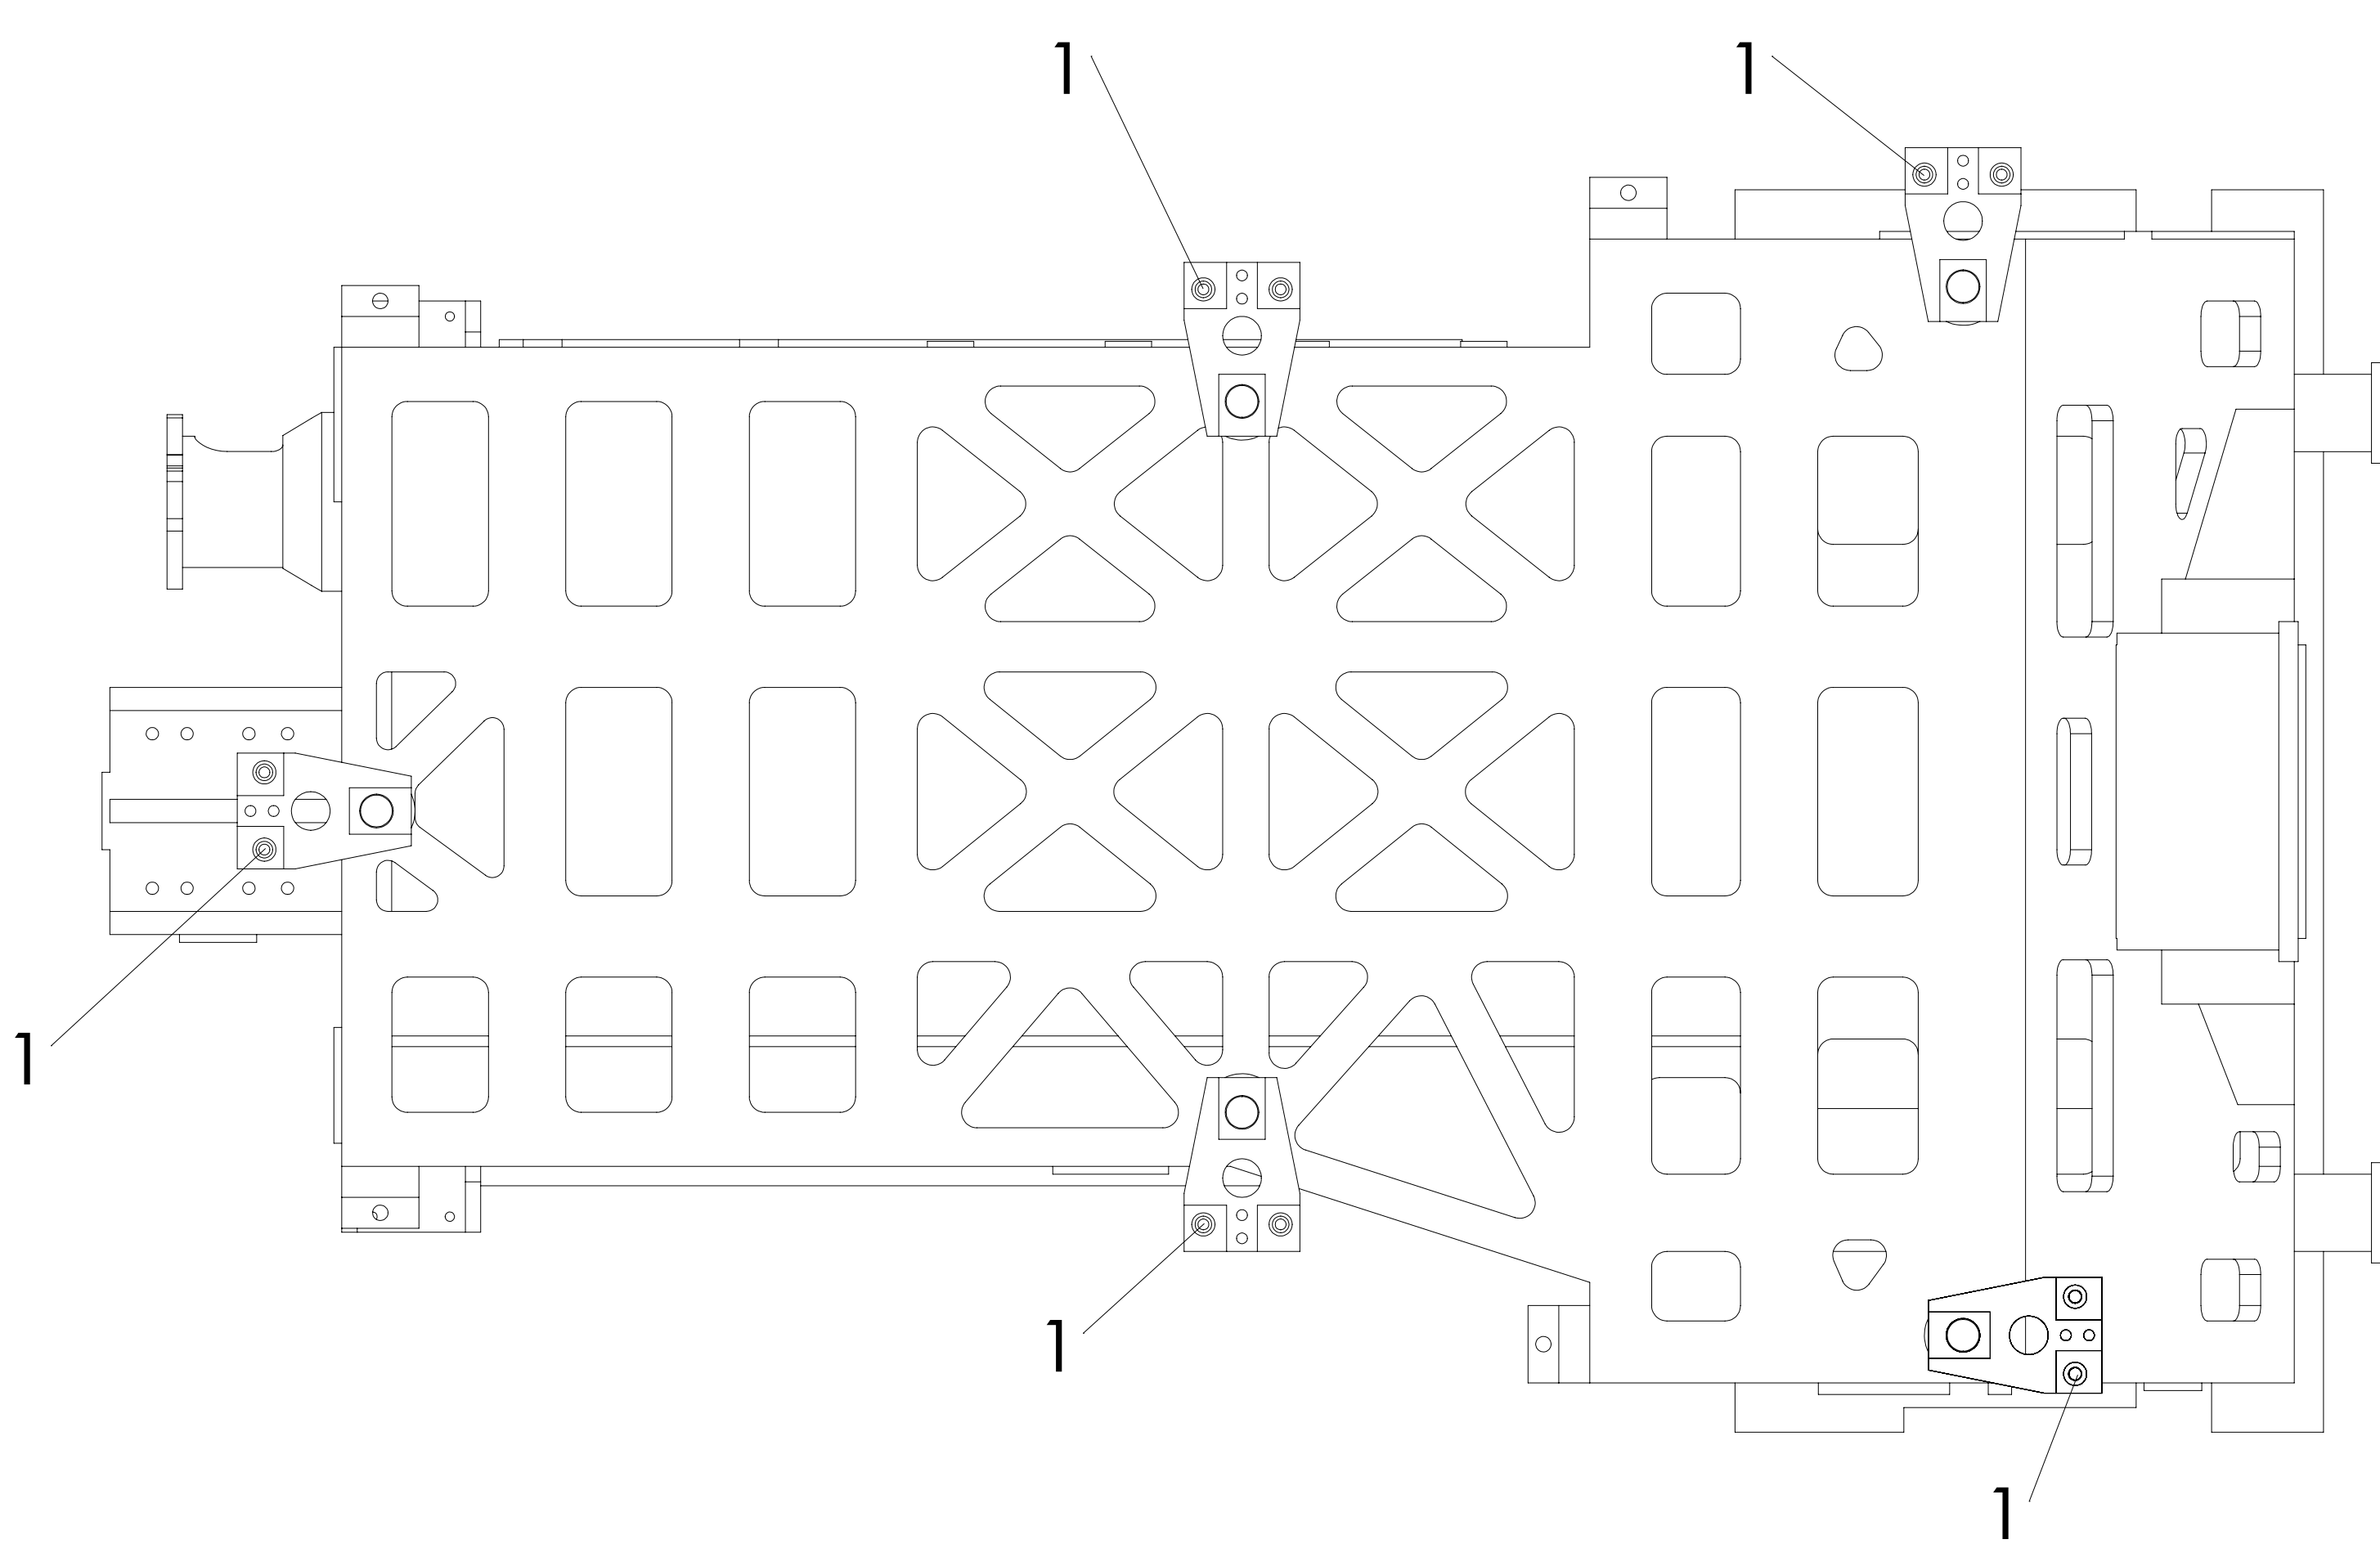


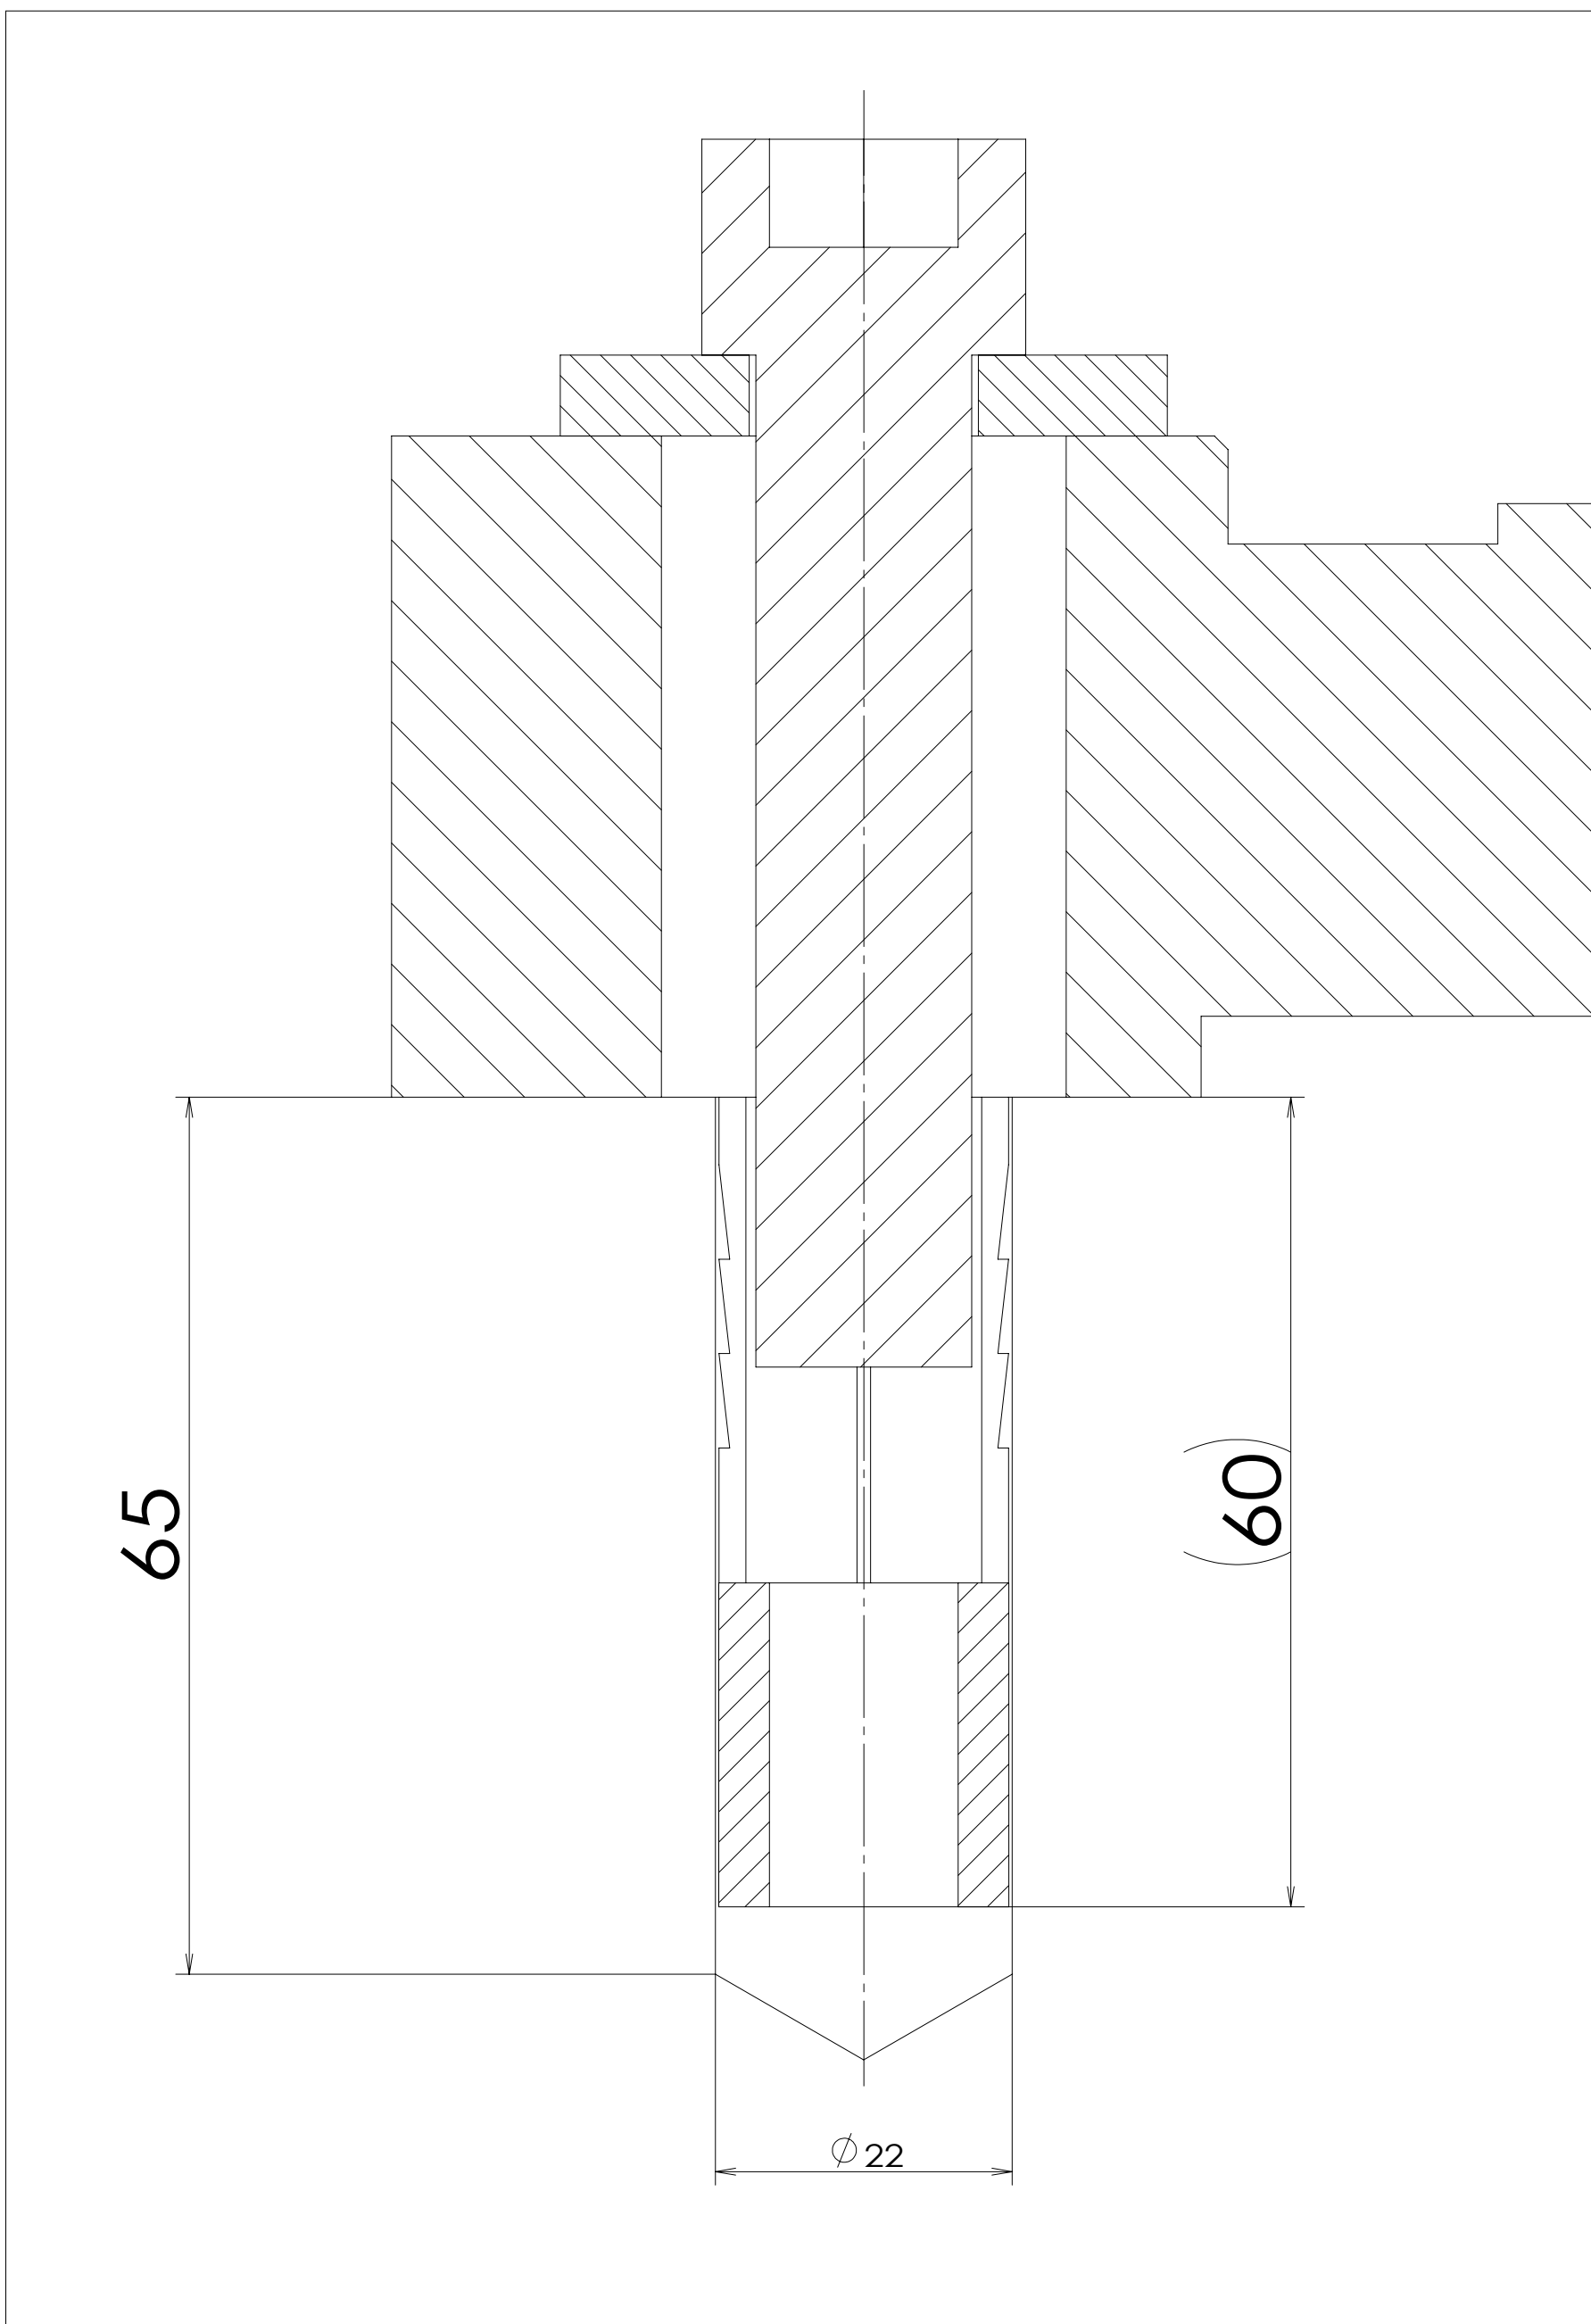

Uplift prevention plate
(1 location for each leveling bolt)
*Pay careful attention to the
mounting dimensions.