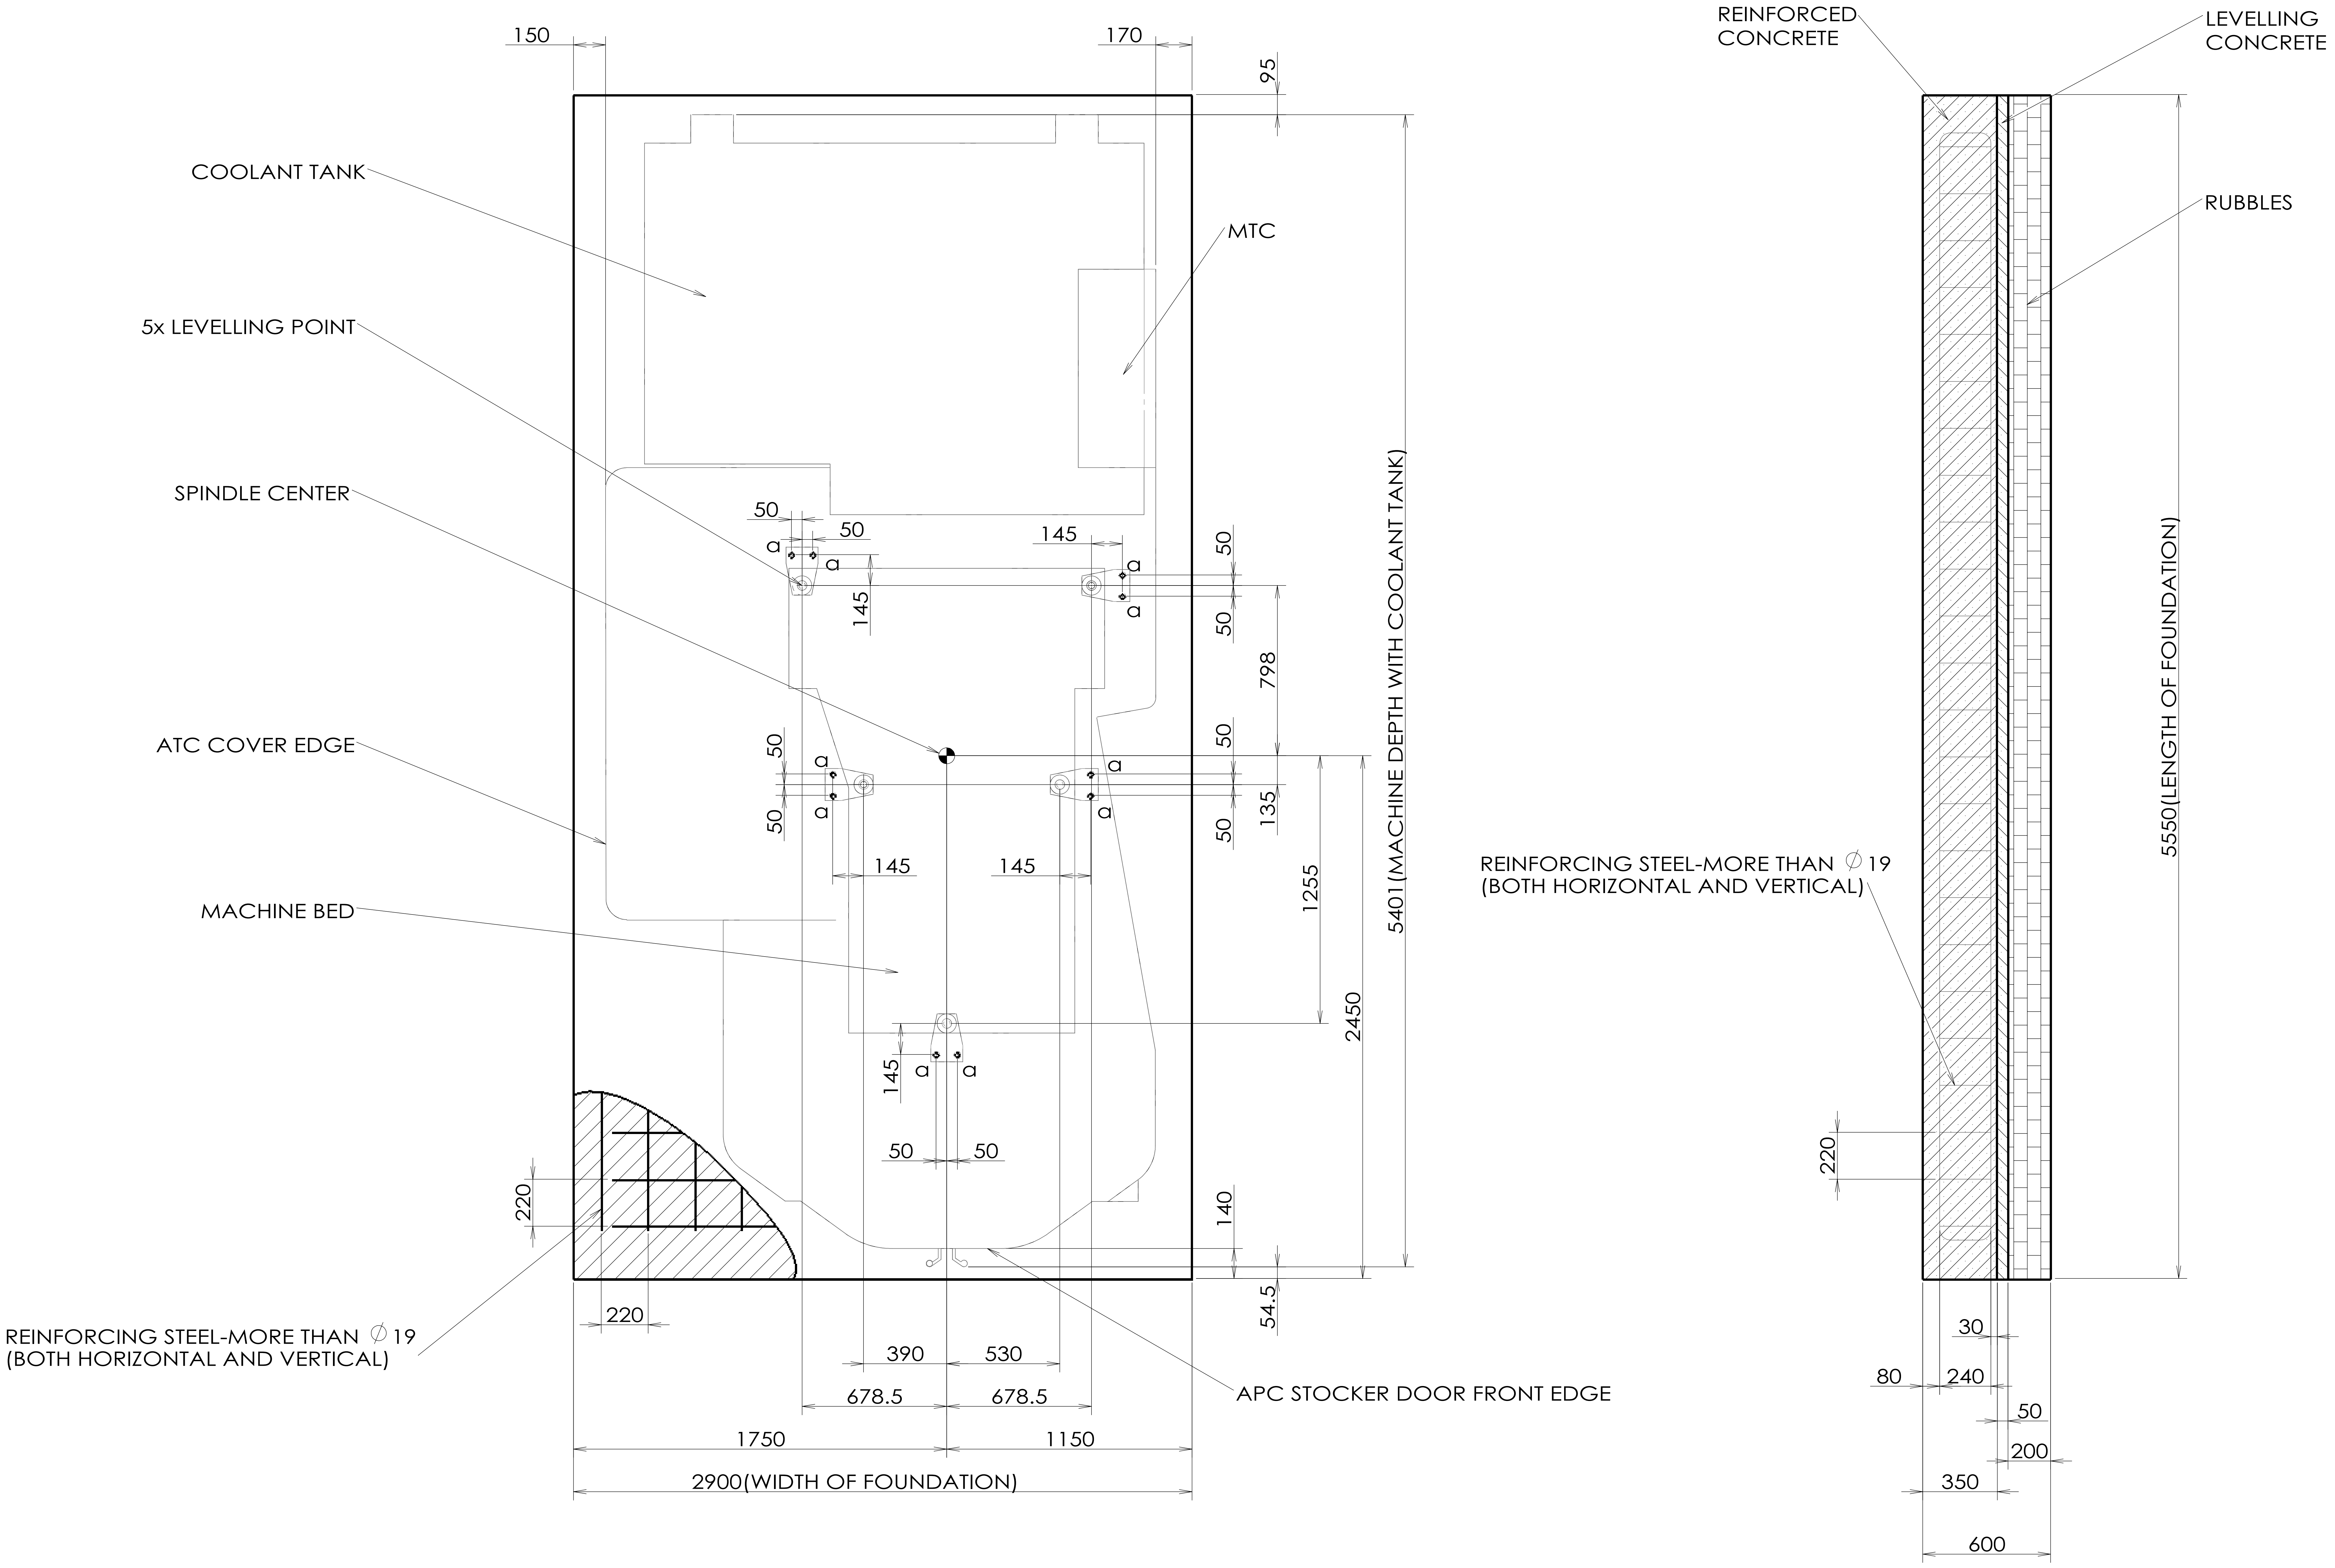
150
170
95
COOLANT TANK
MTC
5x LEVELLING POINT
SPINDLE CENTER
ATC COVER EDGE
MACHINE BED
50
50
145
a
a
a
a
a
a
a
a
a
a
145
50
50
798
50
50
135
50
50
145
145
1255
2450
5401(MACHINE DEPTH WITH COOLANT TANK)
145
50
50
220
140
54.5
220
REINFORCING STEEL-MORE THAN ∅19
(BOTH HORIZONTAL AND VERTICAL)
390
530
678.5
678.5
APC STOCKER DOOR FRONT EDGE
1750
1150
2900(WIDTH OF FOUNDATION)
REINFORCED CONCRETE
LEVELLING CONCRETE
RUBBLES
5550(LENGTH OF FOUNDATION)
REINFORCING STEEL-MORE THAN ∅19
(BOTH HORIZONTAL AND VERTICAL)
220
30
80
240
50
200
350
600